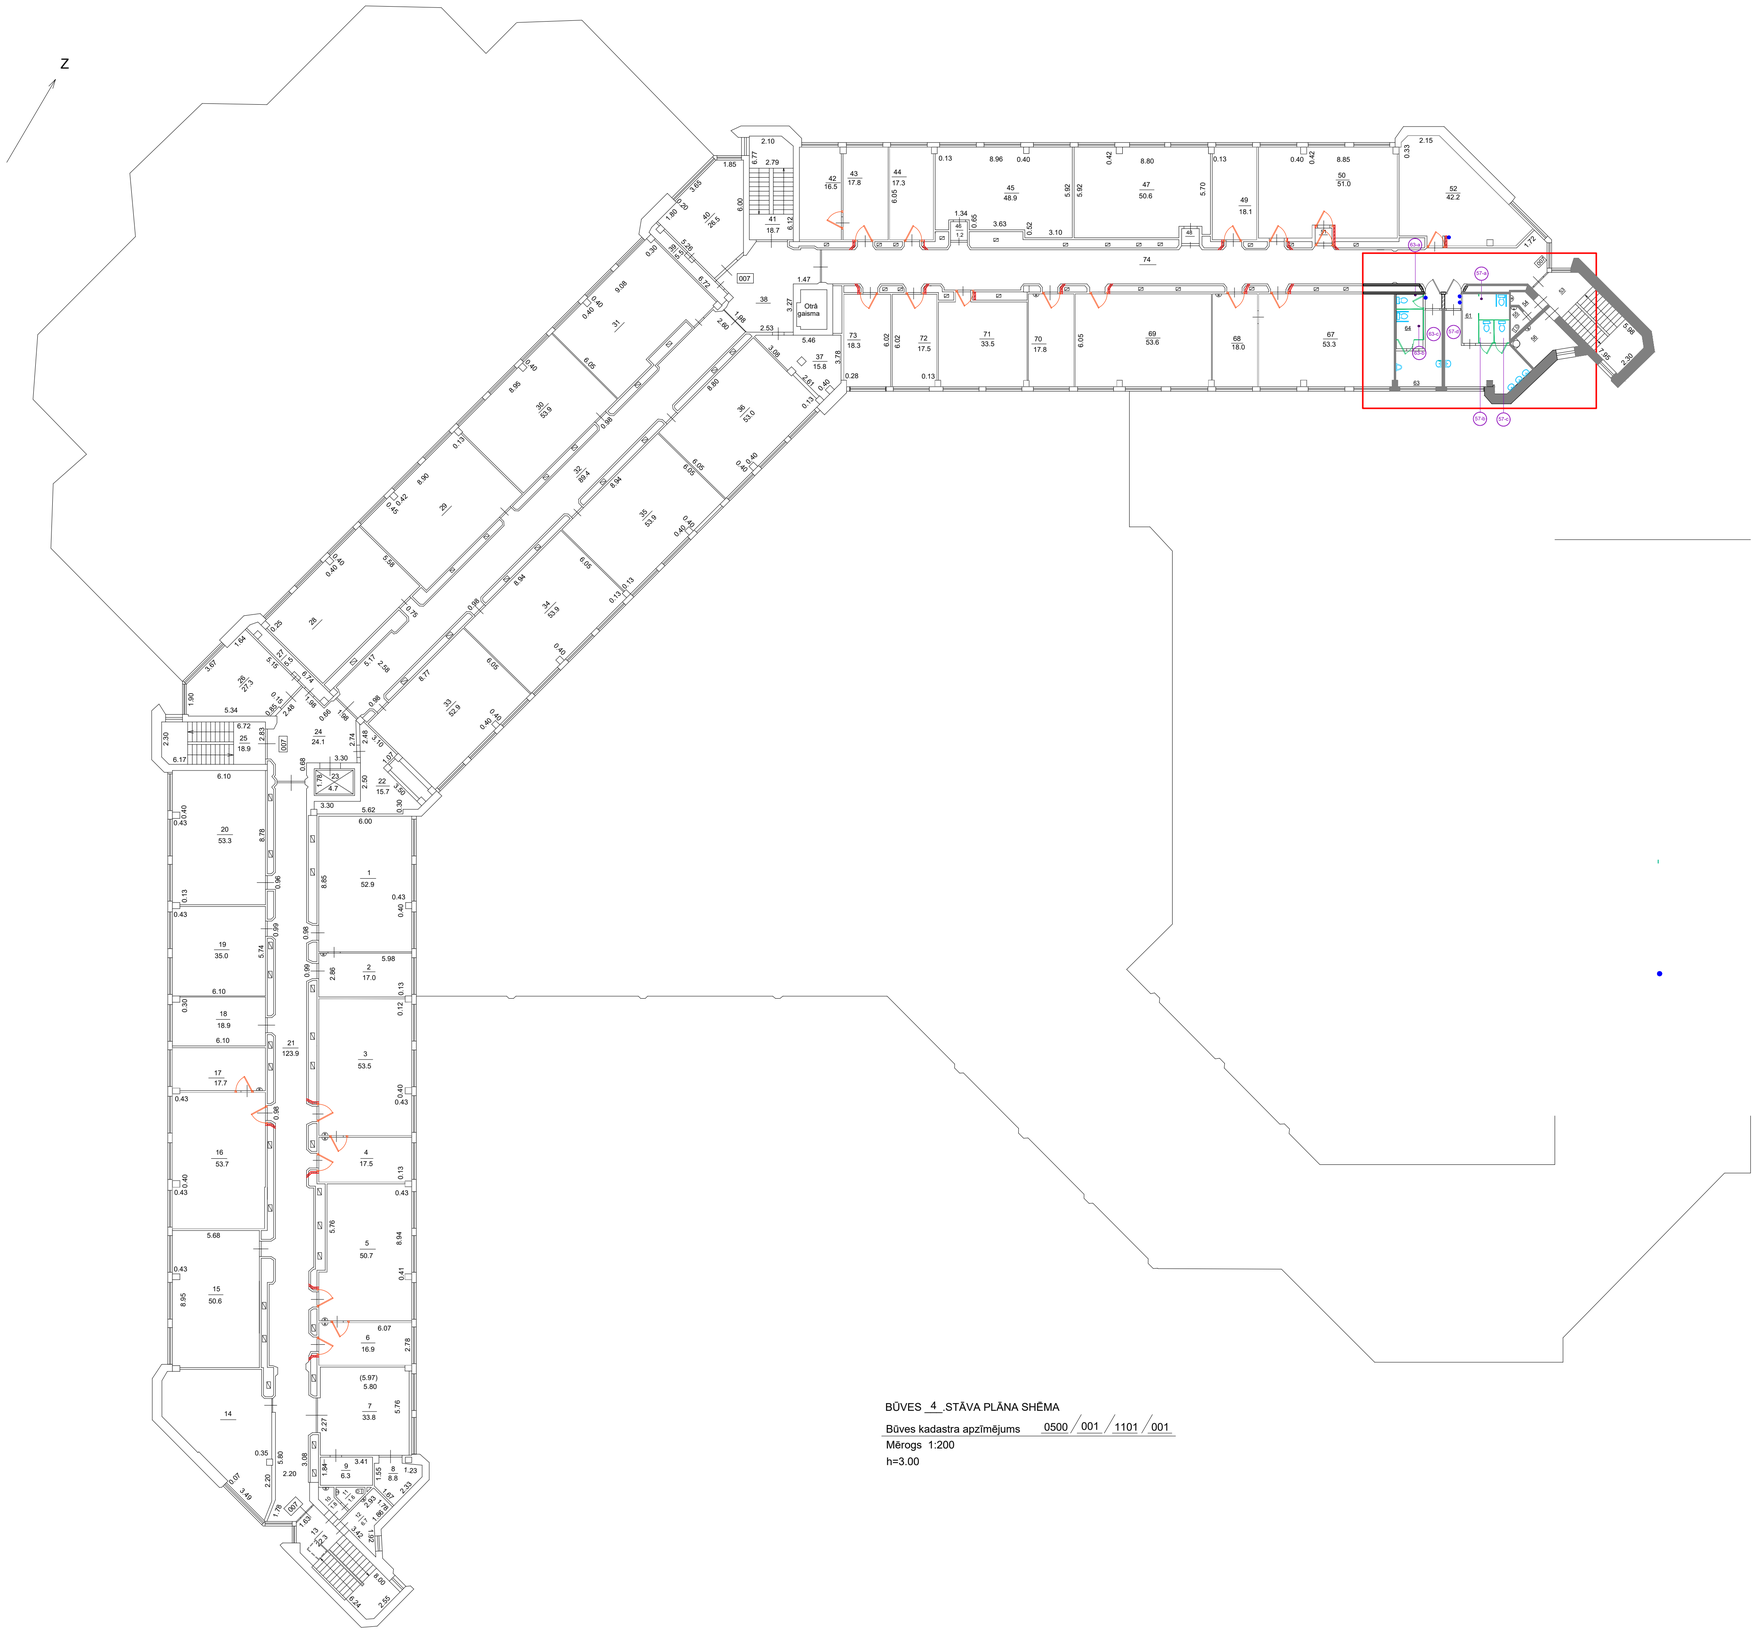

BŪVES 4 STĀVA PLĀNA SHĒMA

Būves kadastra apzīmējums 0500 / 001 / 1101 / 001

Mērogs 1:200

h=3.00

PĒC PĀRPLĀNOŠANAS

Telpas Nr.	TELPAS NOSAUKUMS	Platība m²
57-a	WC invalīdiem	3.4
57-b	WC	1.5
57-c	WC	1.5
57-d	Mazgāšanas telpa	21.6
63-a	WC	1.8
63-b	WC invalīdiem	3.6
63-c	Mazgāšanas telpa	12.7

KODS	IZMAIŅAS	IZM. IZDARĪJA
C		
B		
A		

DARBA RASĒJUMS BŪVNIECĪBAI

IEPRIEKŠEJS MATERIĀLS APSTIPRINĀŠANAI

AUTOCAD RASĒJUMĀ AR ROKU VEIKTAS IZMAIŅAS IR SPĒKĀ, JA APLIECINĀTAS AR BŪVPROJEKTA VADĪTĀJA PARAKSTU.

PROJEKTĒTĀJS:

sia NAMS, Palasta iela 7, LV 1050, Riga, tālr. (+371) 67211076,
fakss (+371) 67221209, e-pasts: nams@nams.arch.lv

NAMS ARHITEKTU BIROJS

PASŪTĪTĀJS: Daugavpils Universitāte
Reģ.Nr. 90000065985, VIENĪBAS IELA 13, DAUGAVPILS, LV-5401

GALVENAIS BŪVUZŅĒMĒJS: SIA „LĀTVIJAS ENERGOCELTNIEKS"
Reģ.Nr. 40103050065, LUBĀNAS IELĀ 43, RĪGA LV-1073

LĪGUMA NR. 14-32/12-1 27.03.2012.

BŪVOBJEKTS: Daugavpils Universitātes Dabaszinātņu un matemātikas fakultātes korpusa renovācija
PARĀDES IELA 1, DAUGAVPILS

FAILA NOS.: EL-12.dwg

ARHĪVA NR.: EL-12.dwg

BŪVE: ESOŠĀ KORPUSA RENOVĀCIJA

DATUMS: 16.07.2012

RASĒJ. NOSAUKUMS: AR APGAISMOJUMA ELEKTROTĪKLIEM

STADIJA: TP

MĒROGS: 1:200

BŪVPR.DAĻAS VAD.:	V.Šmirnova		16.07.2012
IZSTRĀDĀJA:	V.Šmirnova		16.07.2012

DAĻA RAS. NR. EL-12

ŠIS RASĒJUMS TIEK IZSNIEGTS TIKAI KĀ PROJEKTA DOKUMENTĀCIJAS SASTĀVDAĻA. SAŅĒMĒJS PIEKRĪT NEPAVAIROT UN NEIZMAINĪT ŠO RASĒJUMU VAI TĀ DAĻAS BEZ PROJEKTĒTĀJA PIEKRIŠANAS. SAŅĒMĒJS PIEKRĪT, KA ŠIS RASĒJUMS NAV IZMANTOJAMS CITU OBJEKTU PROJEKTĒŠANAI UN CELTNIECĪBAI BEZ SASKAŅOŠANAS AR SIA "NAMS".